


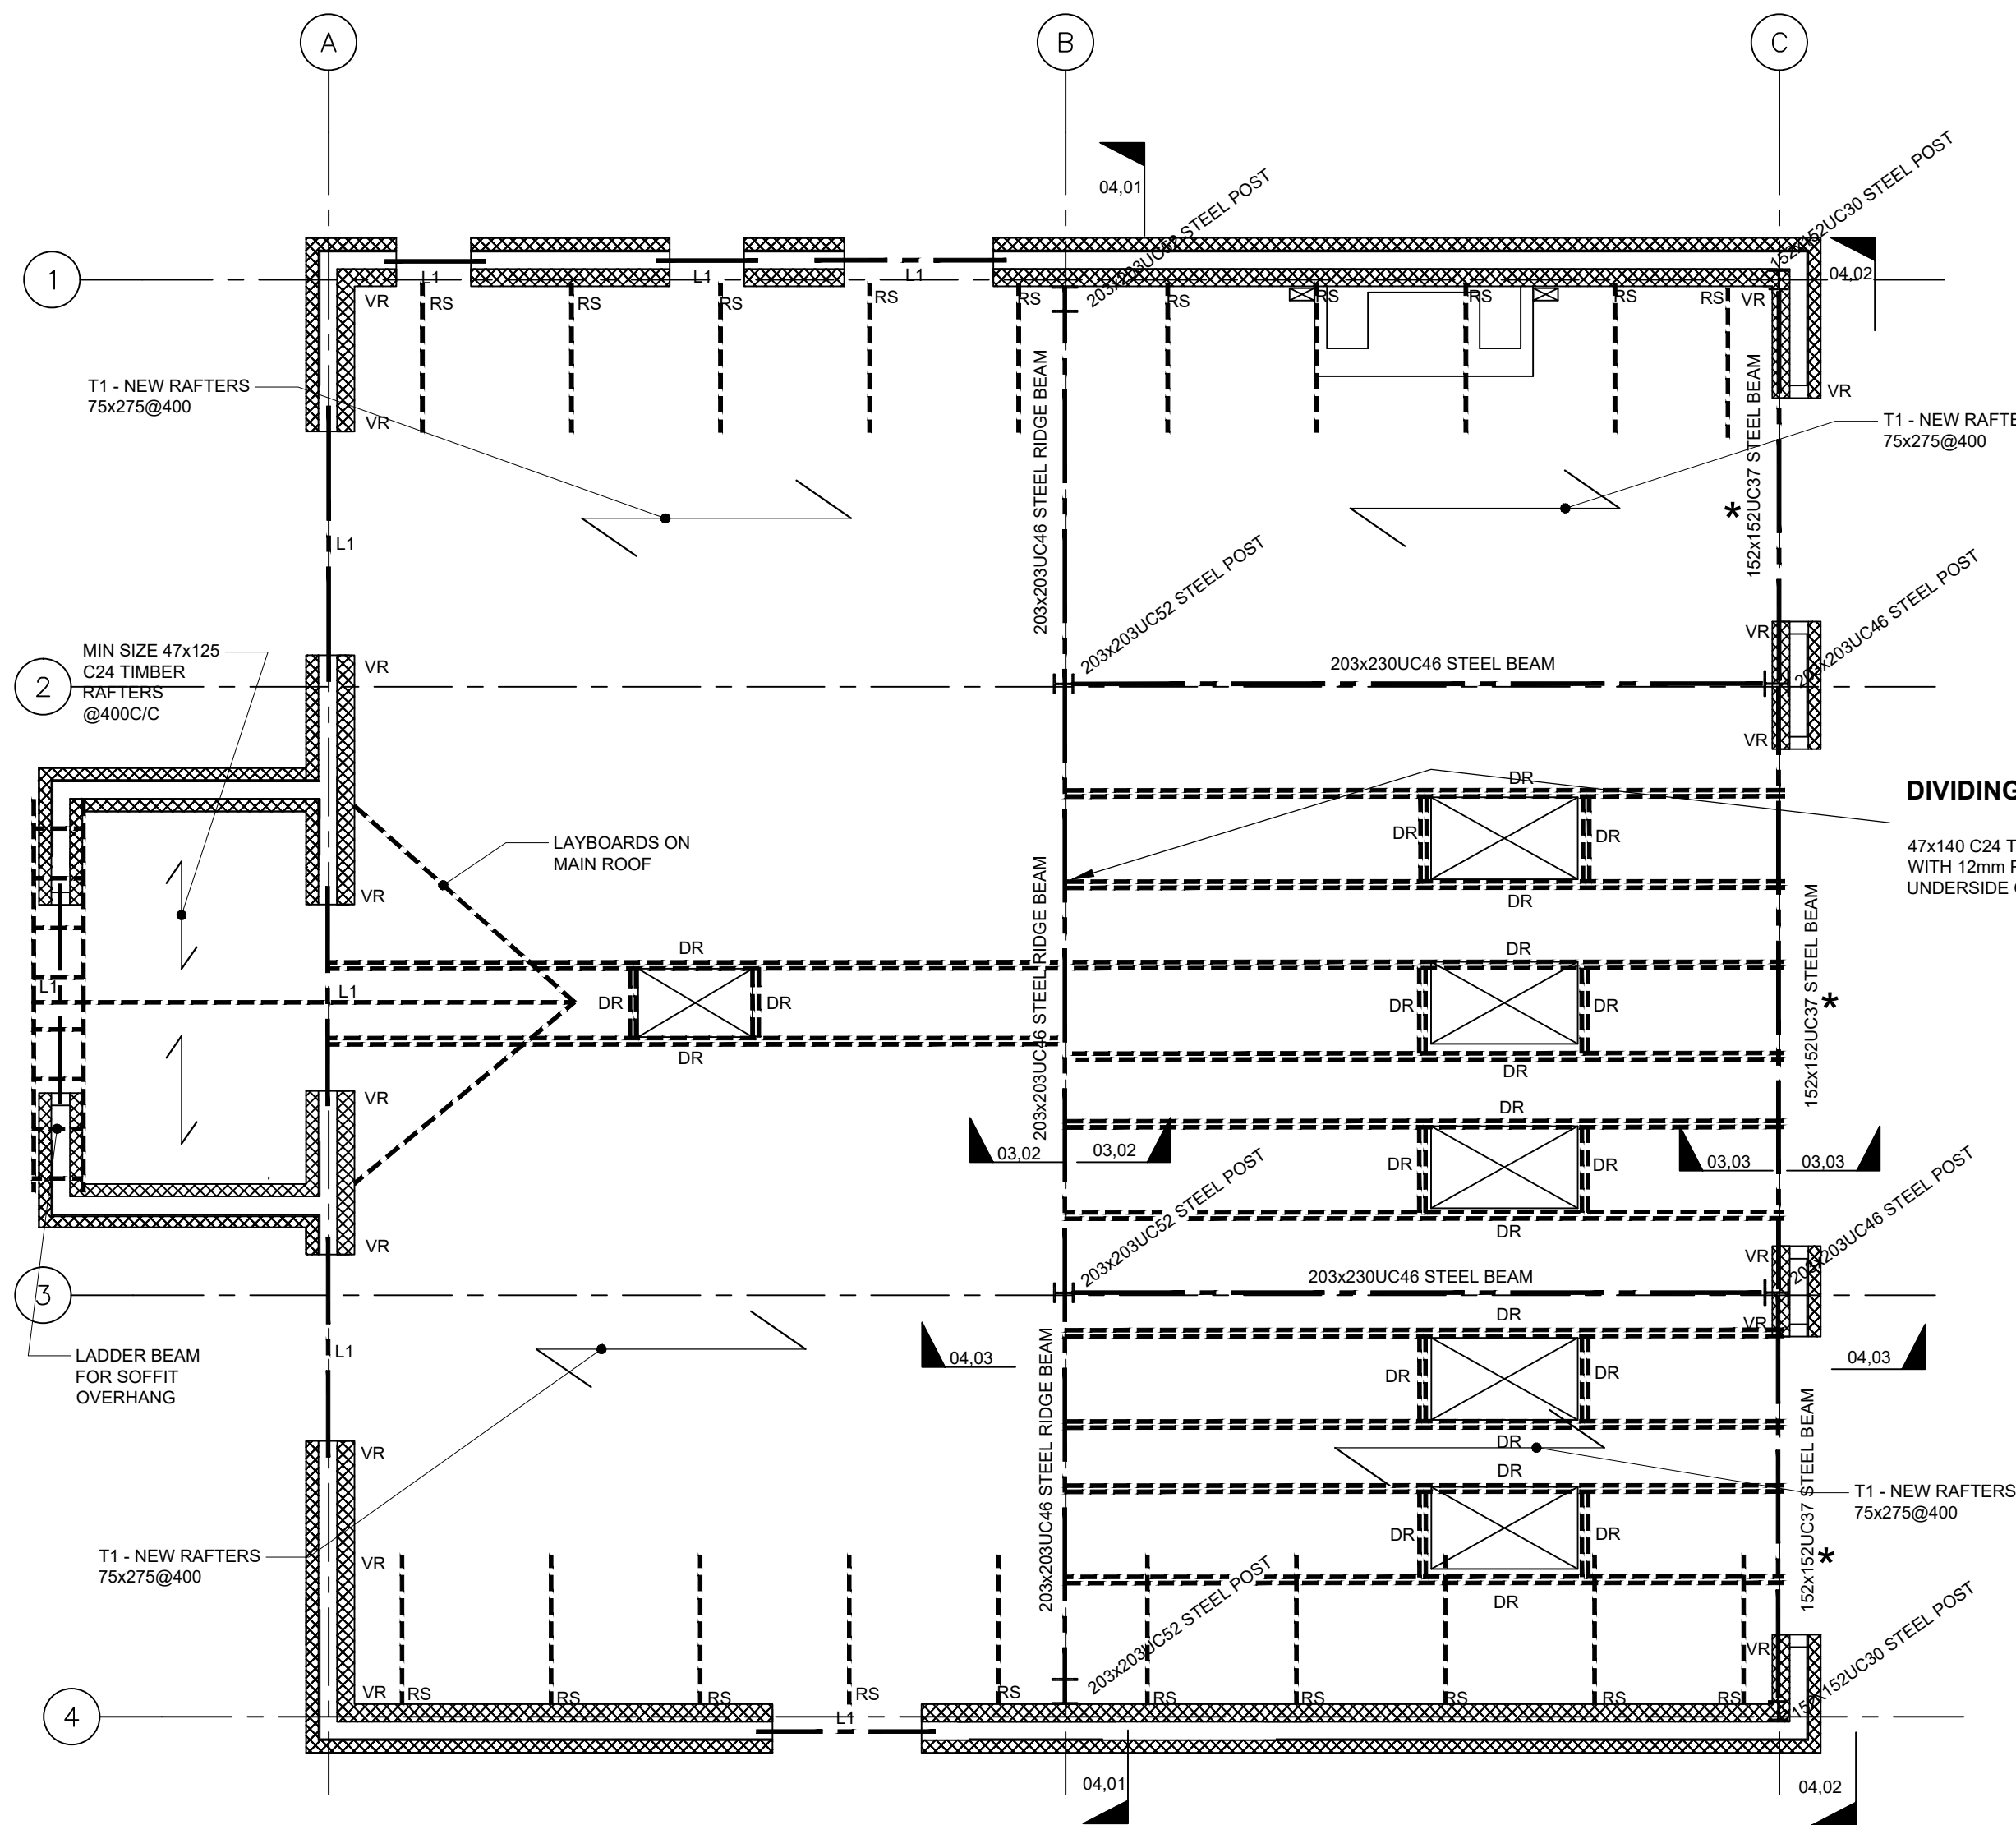

**03,01 ROOF PLAN SHOWING
NEW MEMBERS**

SCALE 1:50

TEMPORARY WORKS TO
MAIN CONTRACTORS
METHOD STATEMENT
DO NOT DIRECTLY SCALE
FROM THIS DRAWING.
USE SITE DIMENSIONS
FOR SETTING OUT AND
ARCHITECTS DRAWINGS

ALL WORK MUST COMPLY WITH THE
CONSTRUCTION (DESIGN AND MANAGEMENT)
REGULATIONS 2015 (CDM 2015)

NOTE DRAWINGS AND CALCULATIONS
ARE ONLY TO COVER PART A OF THE BUILDING
REGULATIONS - ELLIS STRUCTURES HAVE NOT
BEEN APPOINTED AS THE PRINCIPAL DESIGNER
CONTACT OTHERS FOR THIS ROLE

TIMBER MEMBERS

DR = DOUBLE RAFTER 2No 75x275 C24
TIMBERS BOLTED WITH TIMBER LOK
SCREW BOLTS @400C/C


**OPEN BACK CAVITY
LINTELS**

L1 = CG150/125 BY CATNIC OR SIMILAR
(MIN 150mm END BEARING)

RESTRAINT STRAPS


RS - 30x5 PRE BENT GALVANIZED RESTRAINT
STRAPS FIXED OVER 3No RAFTERS WITH SOLID
NOGGINs IN-BETWEEN RAFTERS AND BENT END
DOWN CAVITY HOOKED OVER AND WELL BUILT
IN @1.2M C/C

VR - VERTICAL RESTRAINT STRAPS 30x5 PRE
BENT GALVANISED HOOKED OVER WALL PLATE
AND PLUGGED AND SCREWED TO INNER LEAF
@1.2M C/C AND EACH SIDE OF OPENING

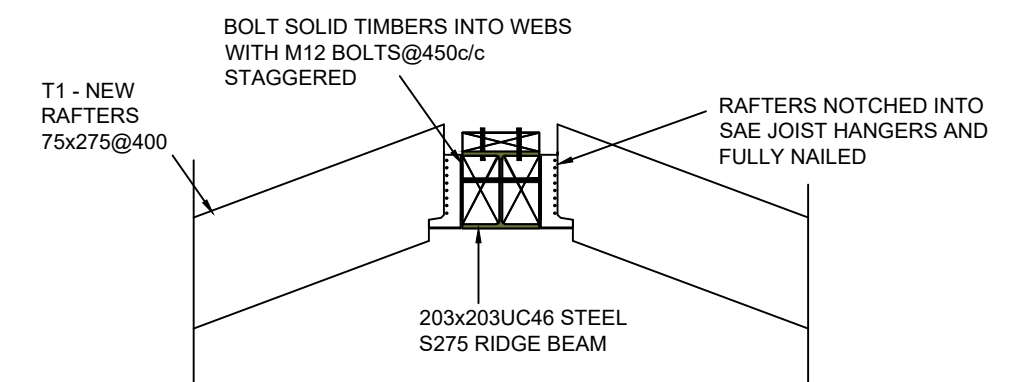

03,02 RIDGE DETAIL

SCALE 1:20

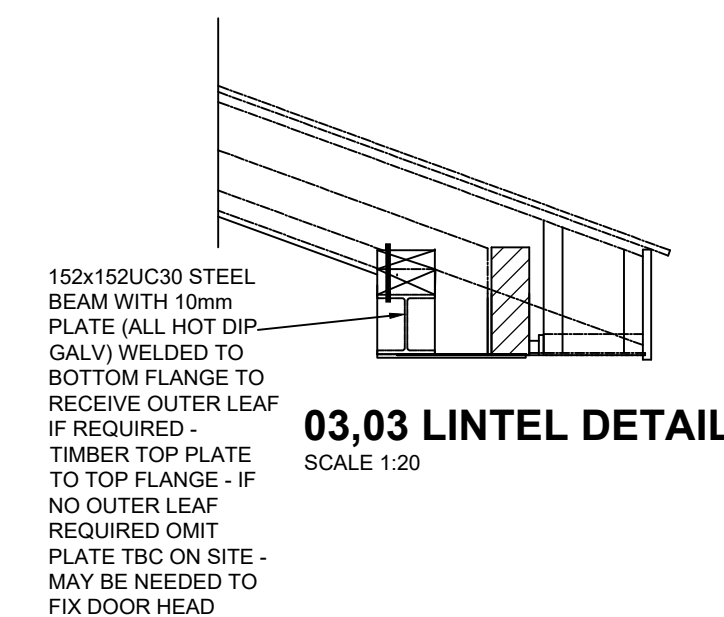

03,03 LINTEL DETAIL

SCALE 1:20

