


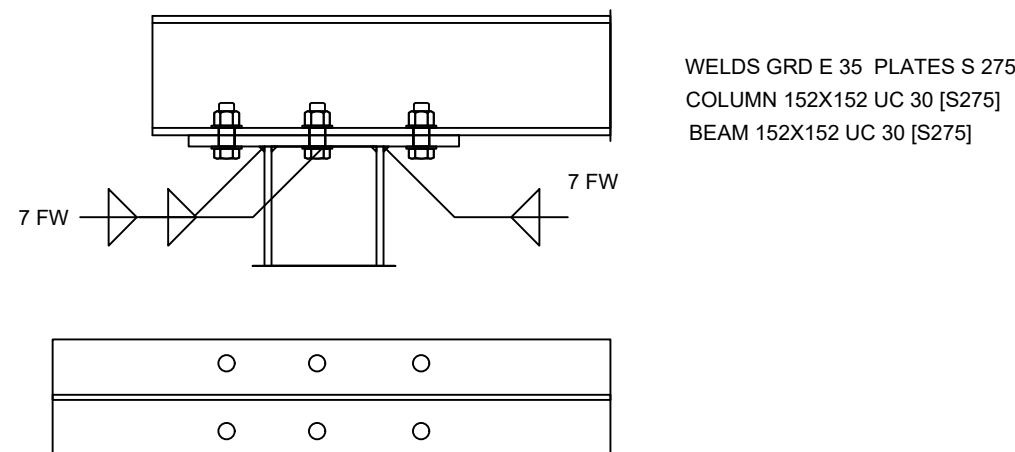


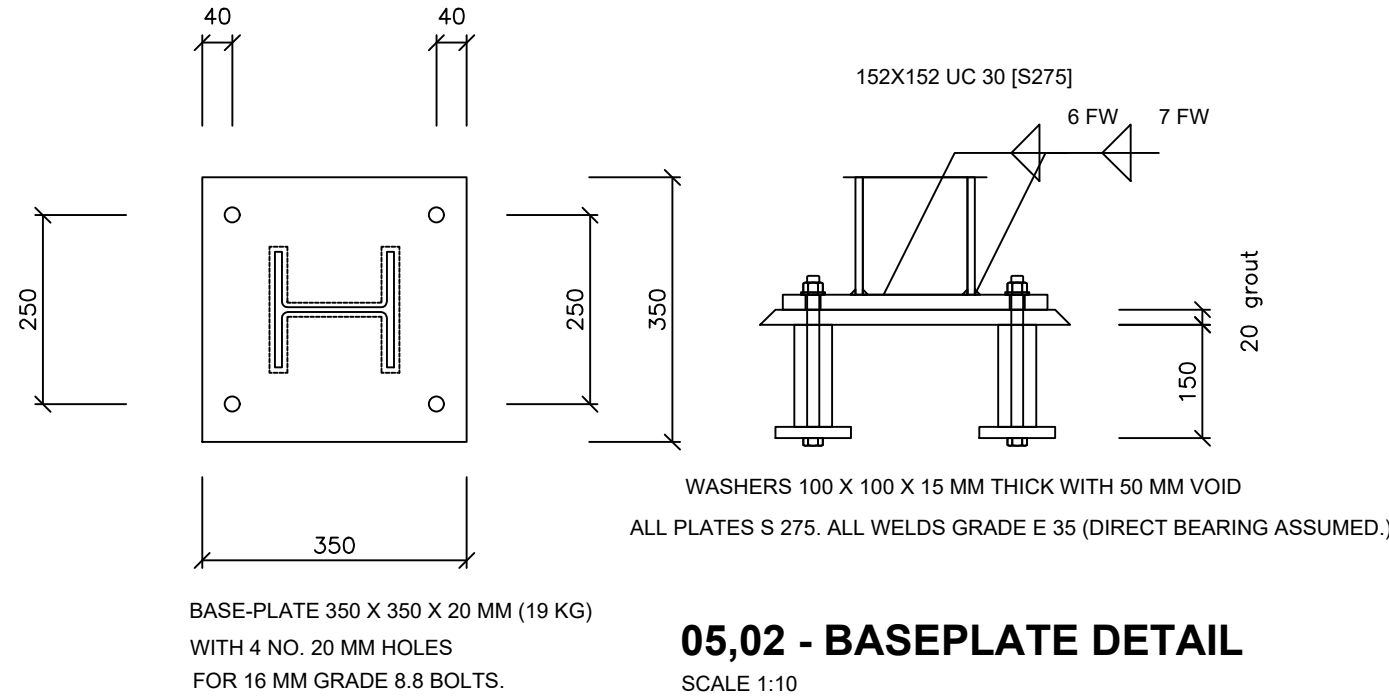

05,04 - CONNECTION DETAIL
SCALE 1:10

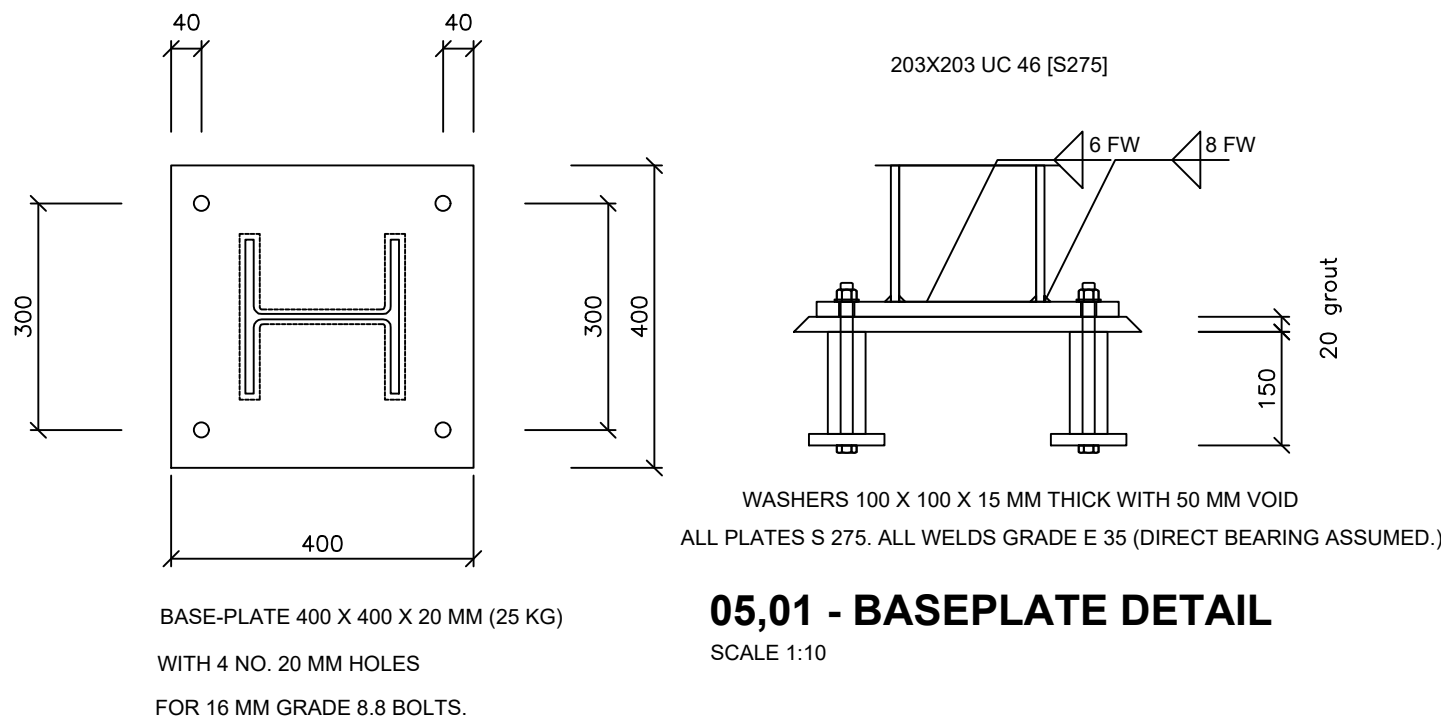

05,05 - CONNECTION DETAIL
SCALE 1:10

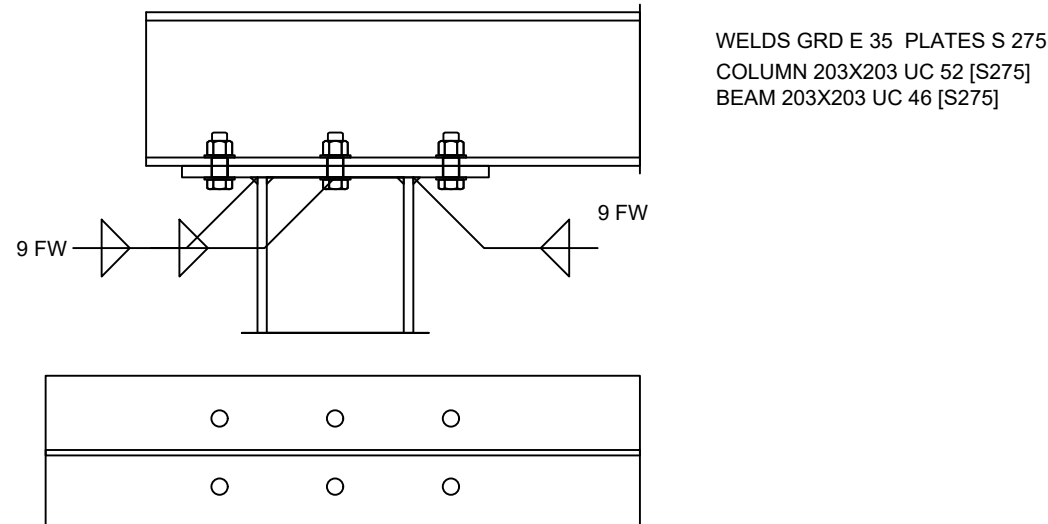