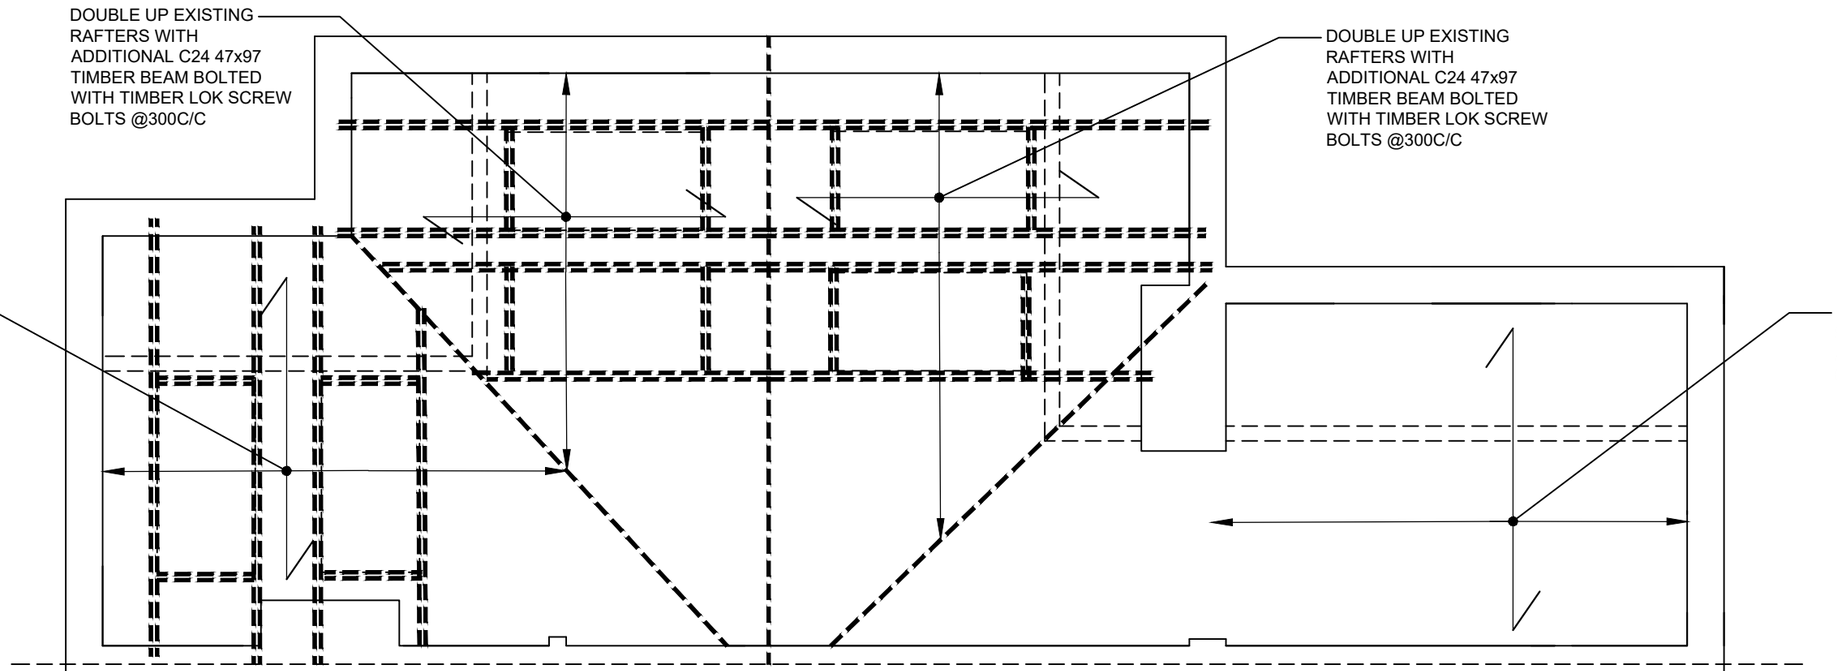


04,01 PROPOSED ROOF FLOOR PLAN SCALE 1:50

ENSURE DOUBLE RAFTER EACH SIDE OF NEW WINDOW POSITIONS TO SUPPORT NEW OPENING

TEMPORARY WORKS TO MAIN CONTRACTORS METHOD STATEMENT

DO NOT DIRECTLY SCALE FROM THIS DRAWING. USE SITE DIMENSIONS FOR SETTING OUT AND ARCHITECTS DRAWINGS

ALL WORK MUST COMPLY WITH THE CONSTRUCTION (DESIGN AND MANAGEMENT) REGULATIONS 2015 (CDM 2015)

JO.